


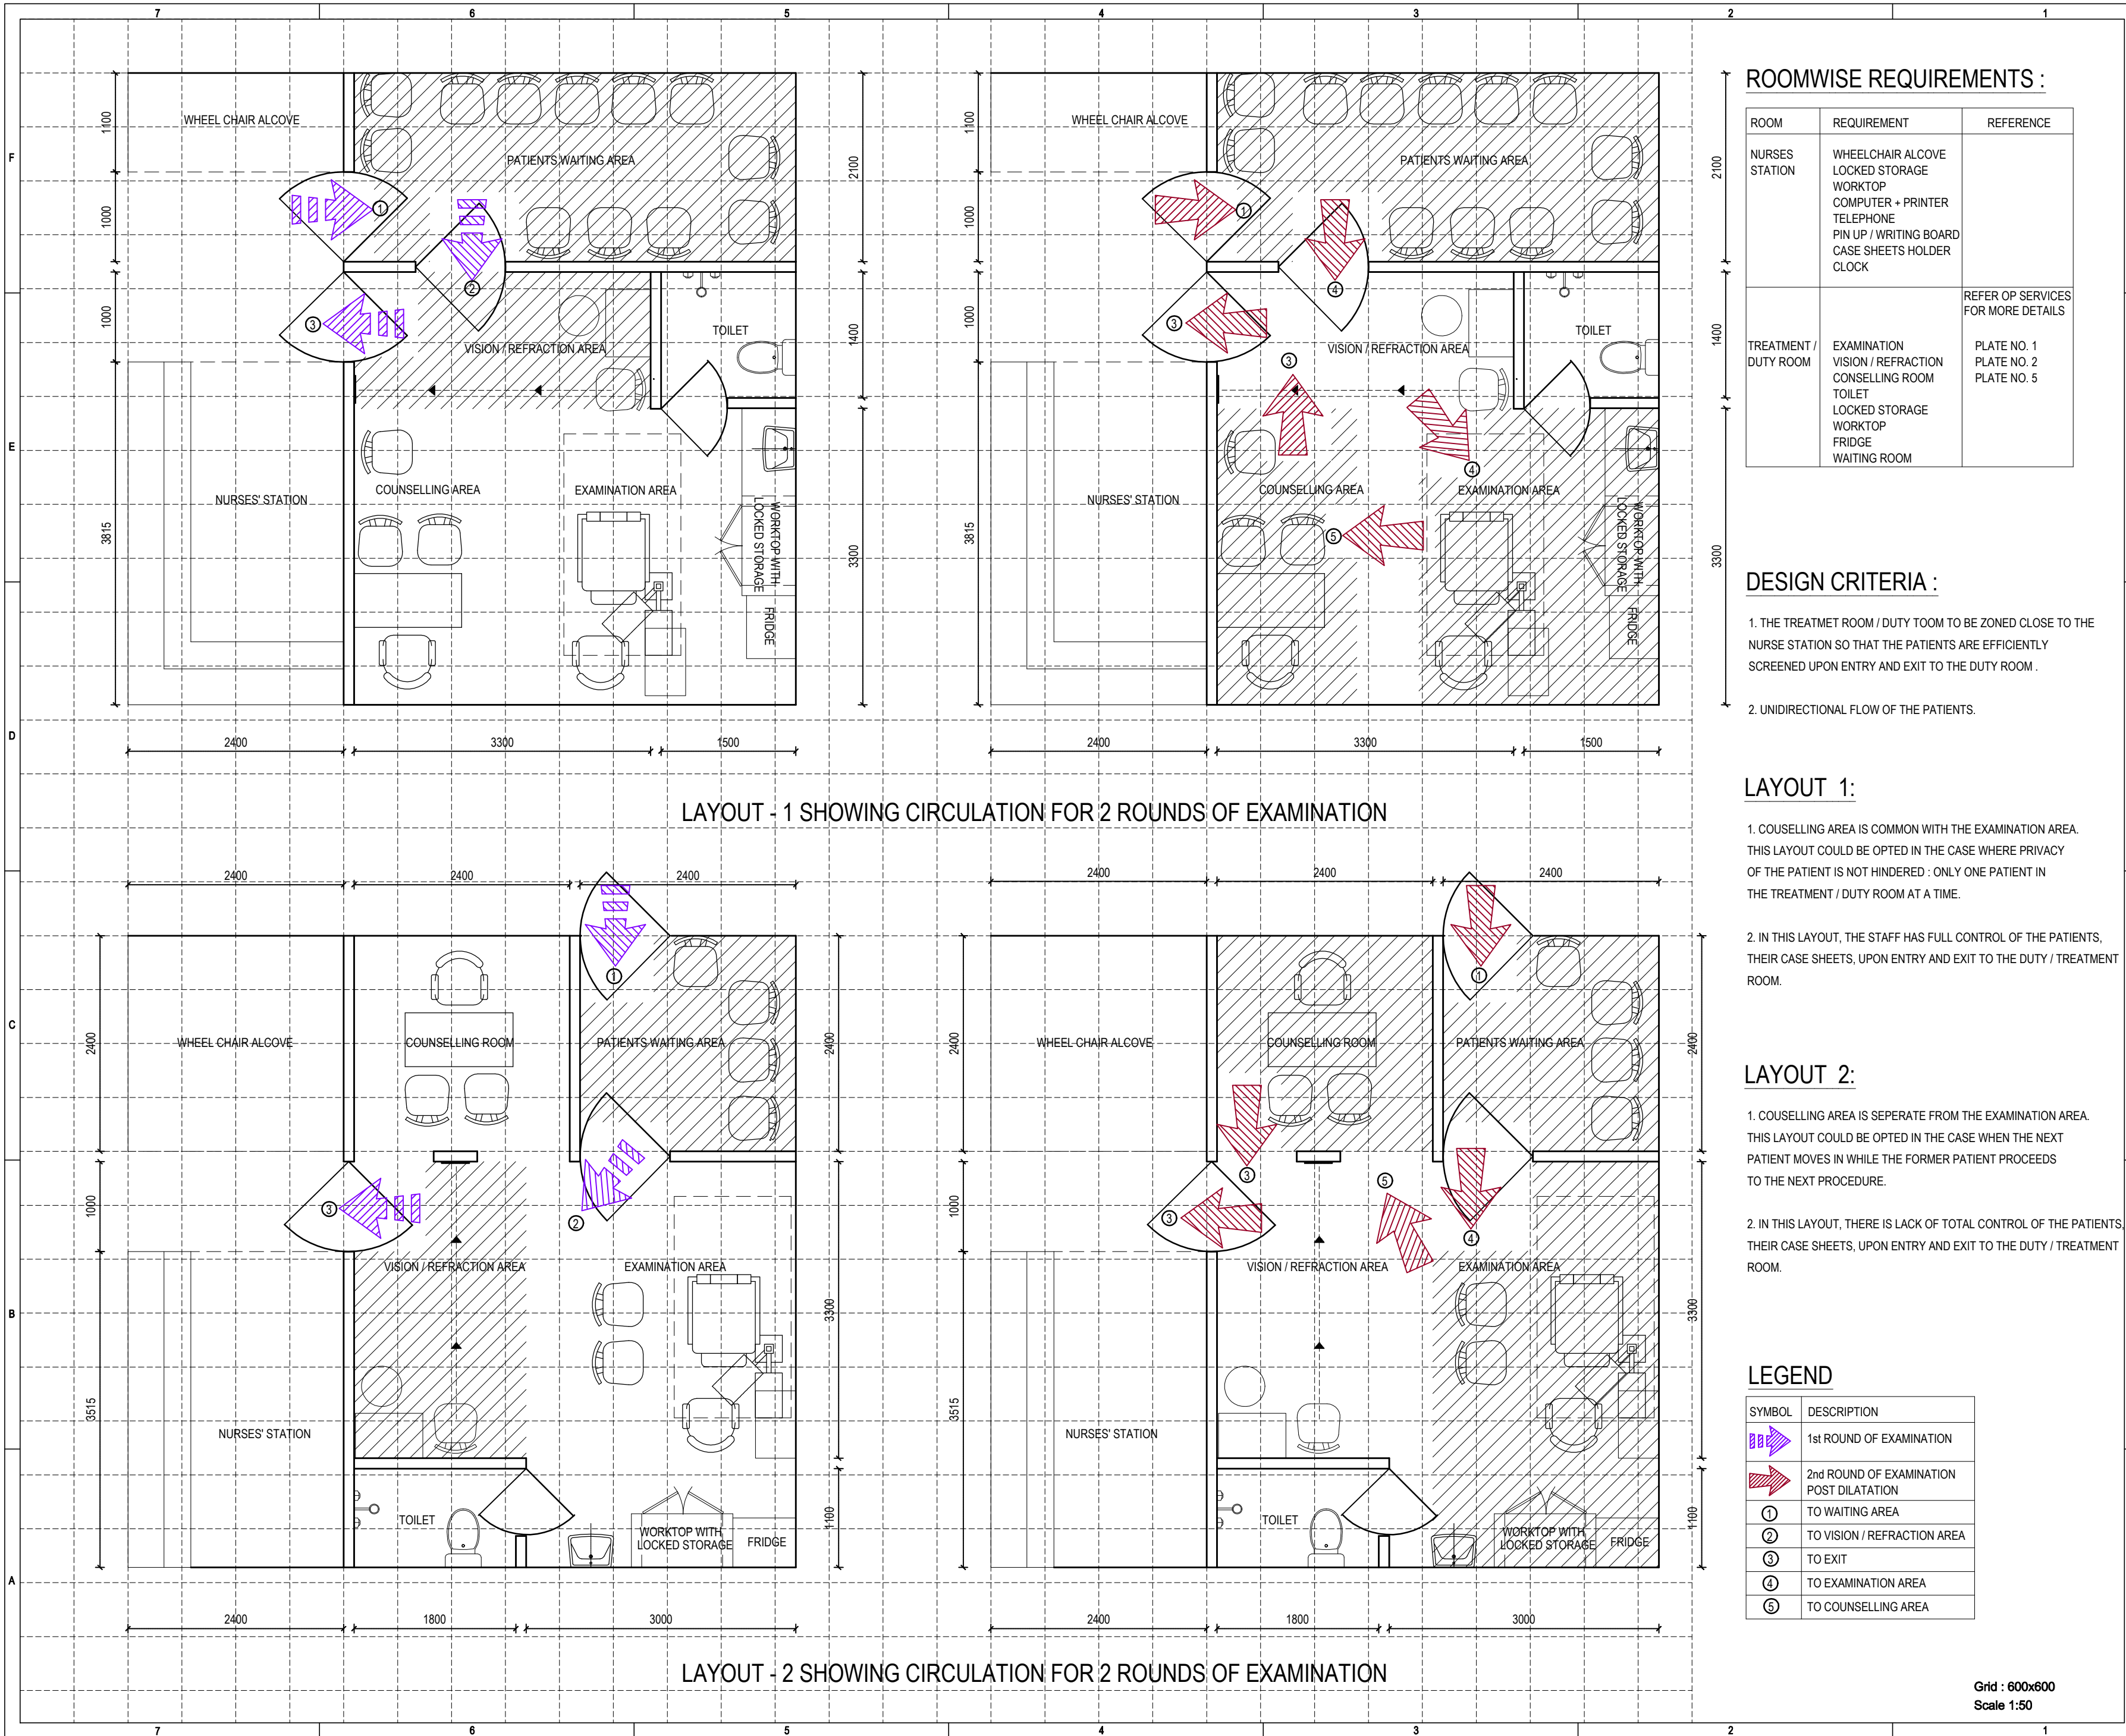

ROOMWISE REQUIREMENTS :

ROOM	REQUIREMENT	REFERENCE
NURSES STATION	WHEELCHAIR ALCOVE LOCKED STORAGE WORKTOP COMPUTER + PRINTER TELEPHONE PIN UP / WRITING BOARD CASE SHEETS HOLDER CLOCK	
TREATMENT / DUTY ROOM	EXAMINATION VISION / REFRACTION CONSELLING ROOM TOILET LOCKED STORAGE WORKTOP FRIDGE WAITING ROOM	REFER OP SERVICES FOR MORE DETAILS PLATE NO. 1 PLATE NO. 2 PLATE NO. 5

DESIGN CRITERIA :

1. THE TREATMET ROOM / DUTY TOOM TO BE ZONED CLOSE TO THE NURSE STATION SO THAT THE PATIENTS ARE EFFICIENTLY SCREENED UPON ENTRY AND EXIT TO THE DUTY ROOM .
2. UNIDIRECTIONAL FLOW OF THE PATIENTS.

LAYOUT 1:

1. COUSELLING AREA IS COMMON WITH THE EXAMINATION AREA. THIS LAYOUT COULD BE OPTED IN THE CASE WHERE PRIVACY OF THE PATIENT IS NOT HINDERED : ONLY ONE PATIENT IN THE TREATMENT / DUTY ROOM AT A TIME.
2. IN THIS LAYOUT, THE STAFF HAS FULL CONTROL OF THE PATIENTS, THEIR CASE SHEETS, UPON ENTRY AND EXIT TO THE DUTY / TREATMENT ROOM.

LAYOUT 2:

1. COUSELLING AREA IS SEPERATE FROM THE EXAMINATION AREA. THIS LAYOUT COULD BE OPTED IN THE CASE WHEN THE NEXT PATIENT MOVES IN WHILE THE FORMER PATIENT PROCEEDS TO THE NEXT PROCEDURE.
2. IN THIS LAYOUT, THERE IS LACK OF TOTAL CONTROL OF THE PATIENTS, THEIR CASE SHEETS, UPON ENTRY AND EXIT TO THE DUTY / TREATMENT ROOM.

LEGEND

SYMBOL	DESCRIPTION
	1st ROUND OF EXAMINATION
	2nd ROUND OF EXAMINATION POST DILATATION
①	TO WAITING AREA
②	TO VISION / REFRACTION AREA
③	TO EXIT
④	TO EXAMINATION AREA
⑤	TO COUNSELLING AREA

Copyright of designs shown herein is retained by this office. Authority is required for any reproduction. Copyright DC Pte. Ltd.

NOTES:

- All dimensions are in mm unless otherwise specified.
- Figured dimensions are to be taken in preference to scale.
- Latest drawing to be followed
- Contractor to verify all dimensions on site before commencing the work.
- Any discrepancies in the drawing to be brought to the notice of consultants before execution.

FOR COMMENTS

REV.	DATE	DESCRIPTION	DWN.	APP.
REVISIONS				

REFERENCES:

ARAVIND EYE HOSPITAL
STANDARDISED ARCHITECTURAL
MODULES

IP SERVICES PATIENT SUPPORT AREAS

LAYOUT AND CIRCULATION

Department	ARCHITECTURAL
Drawn	Brahmani
Dealt	Brahmani
Checked	I.G
Date	28.10.2014

Sheet size A 2

DESIGN COLLABORATIVE

- Architecture
- Planning
- Engineering
- Graphic Design

No.179, III Floor, S.V.Complex, Eswaran koll st., Puducherry-605 001

1240 -A-1 032 R 0

Grid : 600x600
Scale 1:50