

Copyright of designs shown herein is retained by this office. Authority is required for any reproduction.
Copyright DC Pte. Ltd.

- NOTES:
- All dimensions are in mm unless otherwise specified.
 - Figured dimensions are to be taken in preference to scale.
 - Latest drawing to be followed
 - Contractor to verify all dimensions on site before commencing the work.
 - Any discrepancies in the drawing to be brought to the notice of the consultants before execution.

SCHEDULE OF OPENINGS:-

SL.NO.	SYMBOL	DESCRIPTION	WIDTH	HEIGHT
1.	D1	DOUBLE DOOR	2000	2400
2.	D2	DOUBLE DOOR	1800	2400
3.	D3	DOUBLE DOOR	1500	2400
4.	D4	DOUBLE DOOR	1500	2400
5.	D5	DOUBLE DOOR (Electrical room door)	1500	2400
6.	D5a	SINGLE DOOR (Electrical room door)	1000	2400
7.	D6	SINGLE DOOR	1200	2400
8.	D7	SINGLE DOOR	1000	2400
9.	D8	SINGLE DOOR (Terrace - Steel Door)	1000	2100
10.	D9	SINGLE DOOR	900	2100
11.	D10	SINGLE DOOR	800	2100
12.	SSD	DOUBLE DOOR (STAINLESS STEEL - O.T.)	1500	2400
13.	SD1	SHAFT DOOR - DOUBLE DOOR	900	2400/1650
14.	PB	PASSING BOX	900	1650
15.	CG	COLLAPSIBLE GATE	3230	2100
16.	W1	WINDOW	1800	1500
17.	W2	WINDOW	1500	1500
18.	W3	WINDOW	1200	1500
19.	V1	VENTILATOR	1800	600
20.	V2	VENTILATOR	600	750
21.	V3	VENTILATOR	450	750
22.	V4	VENTILATOR	1500	600
23.	LO	LIFT OPENING	900	2100
24.	JW	JAALI WORK (RAMP)	2000	1250

AREA STATEMENT

GROUND FLOOR AREA - 815.00 Sqmt
FIRST FLOOR AREA - 820.00 Sqmt
PORCH AREA - 120.00 Sqmt
FIRST FLOOR SERVICE AREA - 92.00 Sqmt

FOR CONSTRUCTION

R5	09.01.2019	REVISED CLOUD AREA	R.Abi	V.K
R4	10.12.2018	REVISED CLOUD AREA-R4 SCHEDULE OF OPENING AND SHAFT CLOUD AREA REVISED.	R.Abi	V.K
R3	29.09.2018	REVISED CLOUD AREA AND SCHEDULE OF OPENING	R.Abi	V.K
R2	20.09.2018	REVISED LAYOUT	R.Abi	V.K
R1	26.07.2018	REVISED LIFT COLUMN & WINDOWS HEIGHT	R.Abi	V.K
REV.	DATE	DESCRIPTION	DWN.	APP.
		REVISIONS		

REFERENCES:

ARAVIND EYE HOSPITAL - KOVILPATTI
HOSPITAL BLOCK

GROUND FLOOR PLAN

ARCHITECTURAL TENDER DRAWING

Department Architectural
Drawn R.Abi
Deall I.G.
Checked I.G.
Date 12.07.2018


Sheet size A1

DESIGN COLLABORATIVE

• Architecture
• Planning
• Engineering
• Graphic Design

No.179, III Floor, S.V.Complex, Eswaran kollu st., Pudukcherry-605001

1214 -A-1- 001 R 5

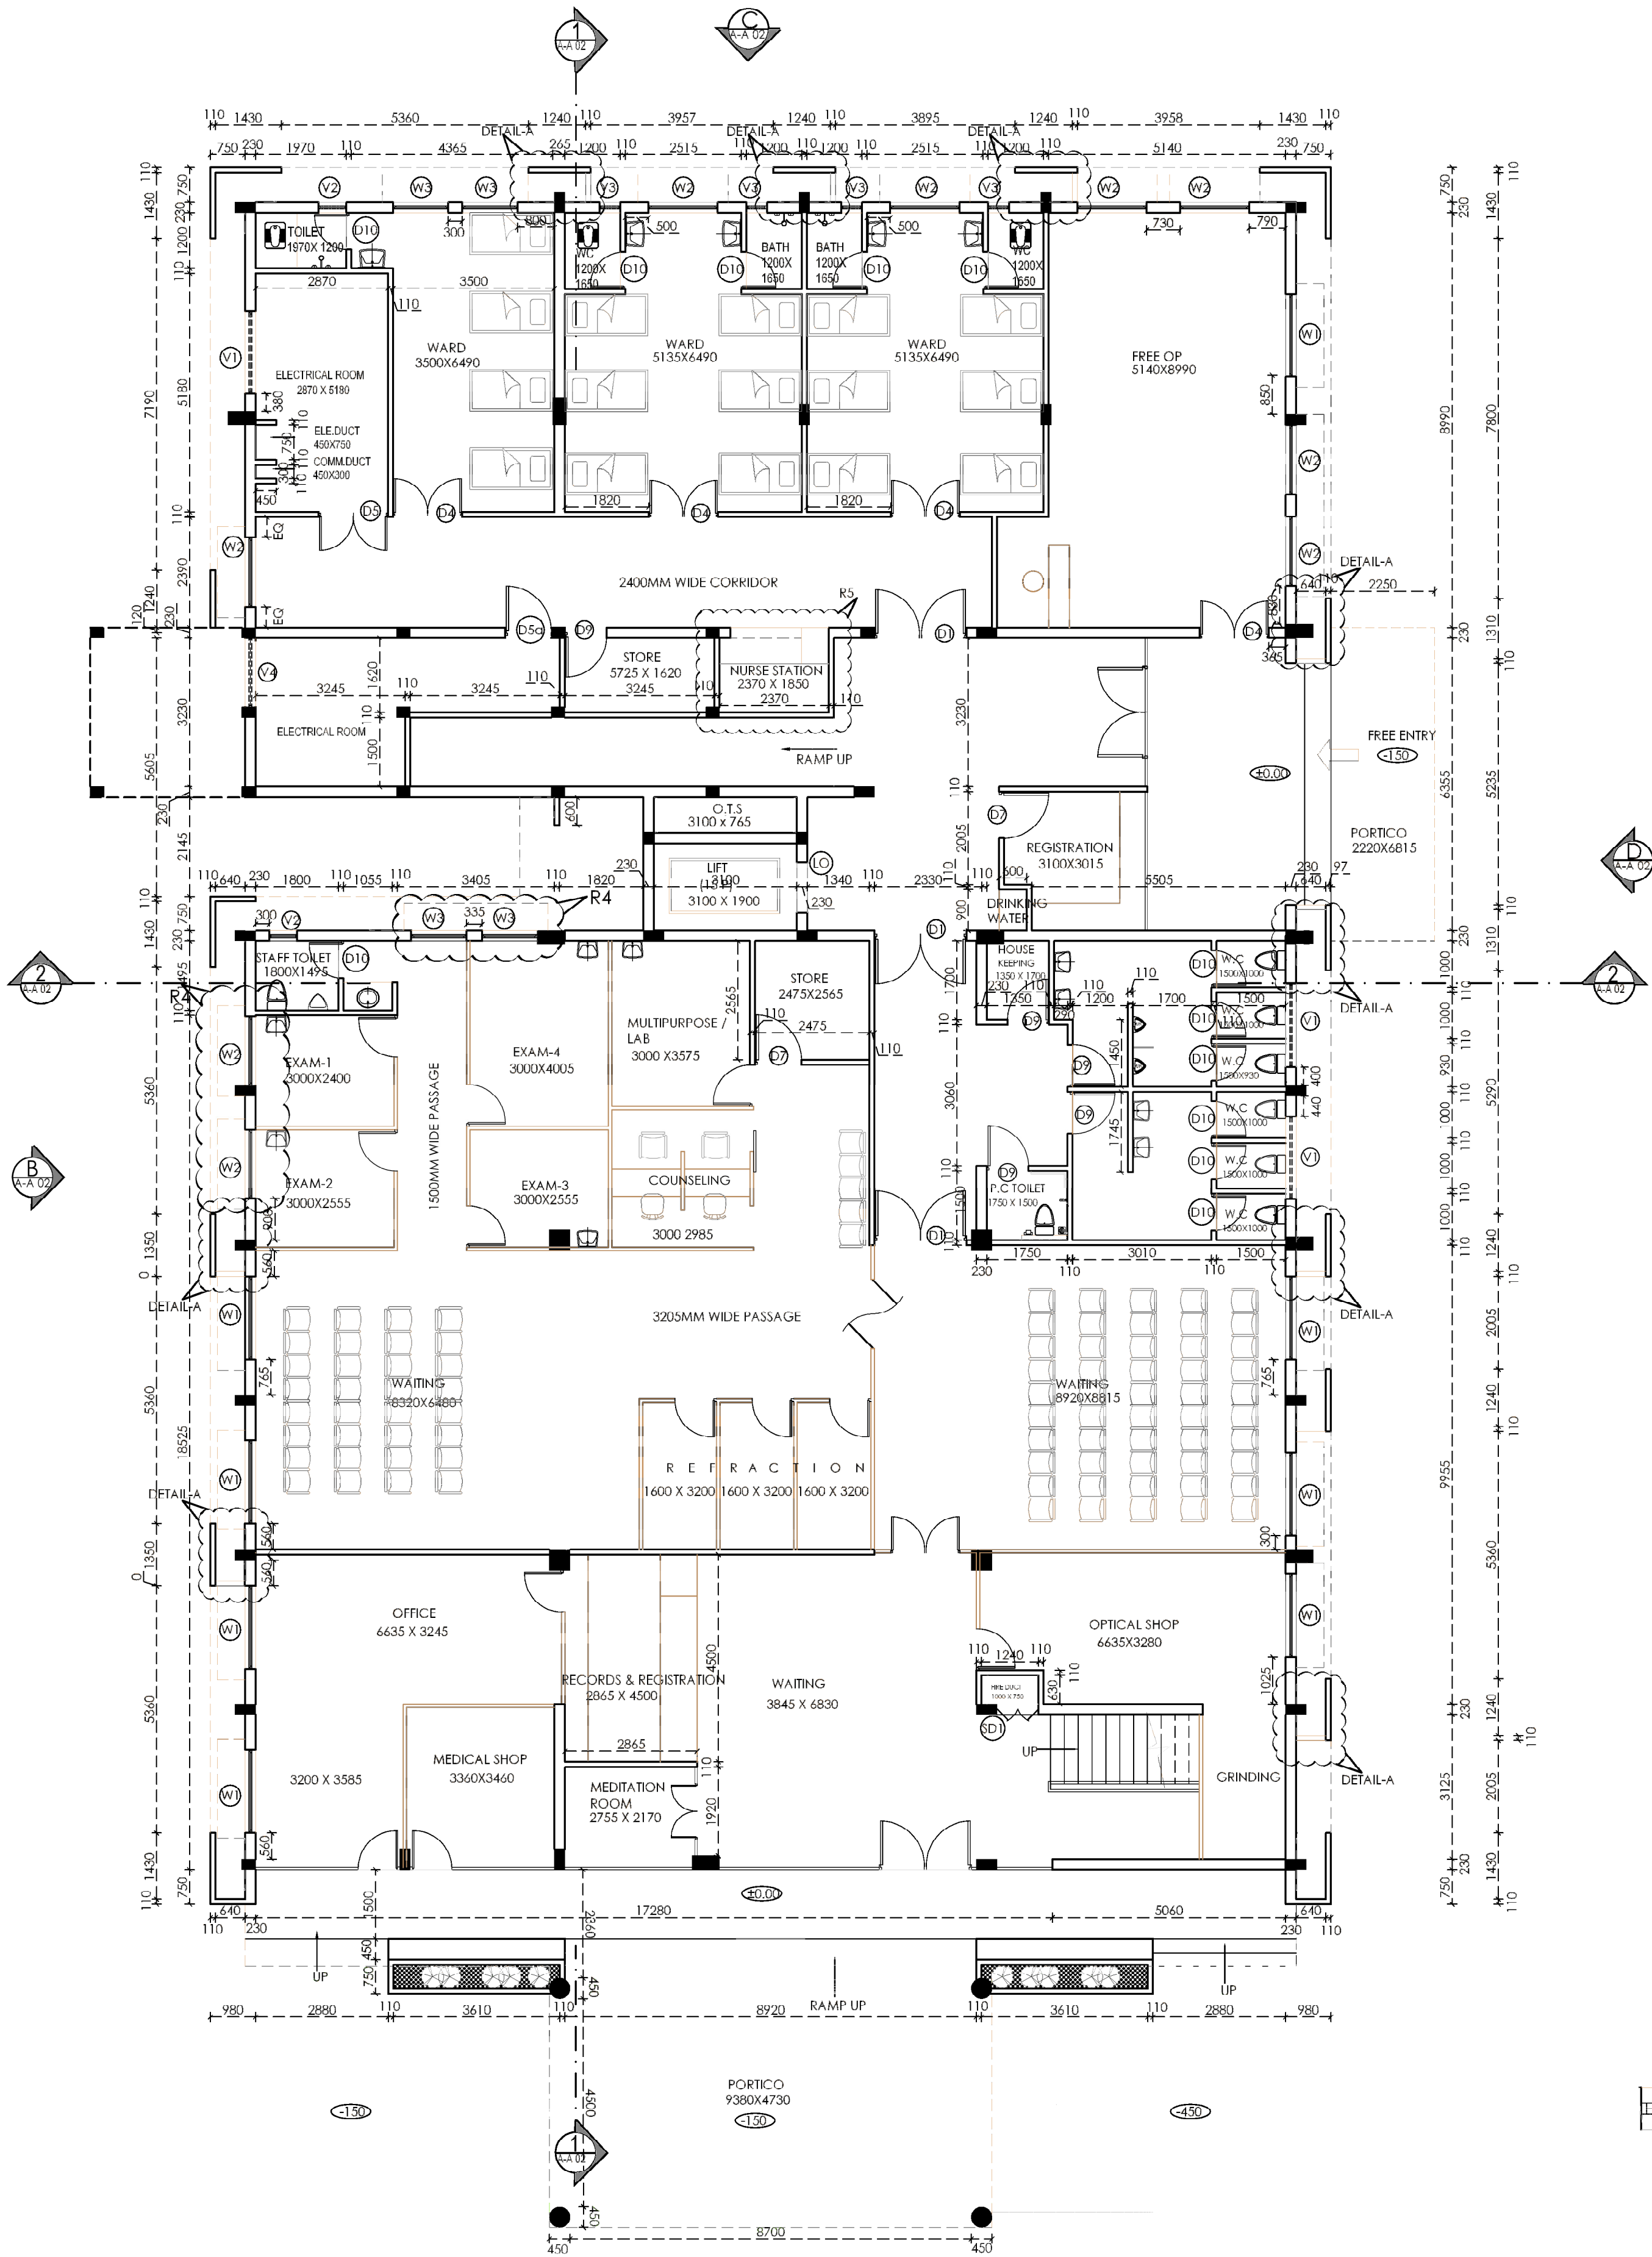

GROUND FLOOR PLAN

SECTION-3
(SCALE 1:25)

ELEVATION-E
(SCALE 1:25)

DETAIL- A
(SCALE 1:25)

SCALE 1:100