


OT complex design that involves two levels

A model to consider when there is:


- A need to allocate a larger space for the operating rooms
- Limited carpet area available for space planning

CSSD located on a different level than the OT complex;
transfers sterile supplies to the operating rooms and receives
soiled through two separate shunts

The image is a detailed architectural floor plan of a hospital wing. The plan includes various rooms such as 'FREE IP PATIENT LIFT', 'OPD LIFT-2', 'STAIRCASE - 2', 'ATTENDERS WAITING', 'NURSE STATION', 'DAYCARE & INPATIENT PRE-PREPARATION', 'VIP CABIN', 'AIR LOCK - 2.4 M WIDE CORRIDOR', 'STERILE STORE', 'INSTRUMENTS WASHING', 'ETO STERILIZATION', and 'ELECTRICAL PANEL ROOM'. A red rectangular box highlights a specific area on the right side of the plan, which is labeled 'CSSD' in a purple box. The plan also shows various corridors, stairs, and service areas. Dimensions and room numbers are indicated throughout the drawing.

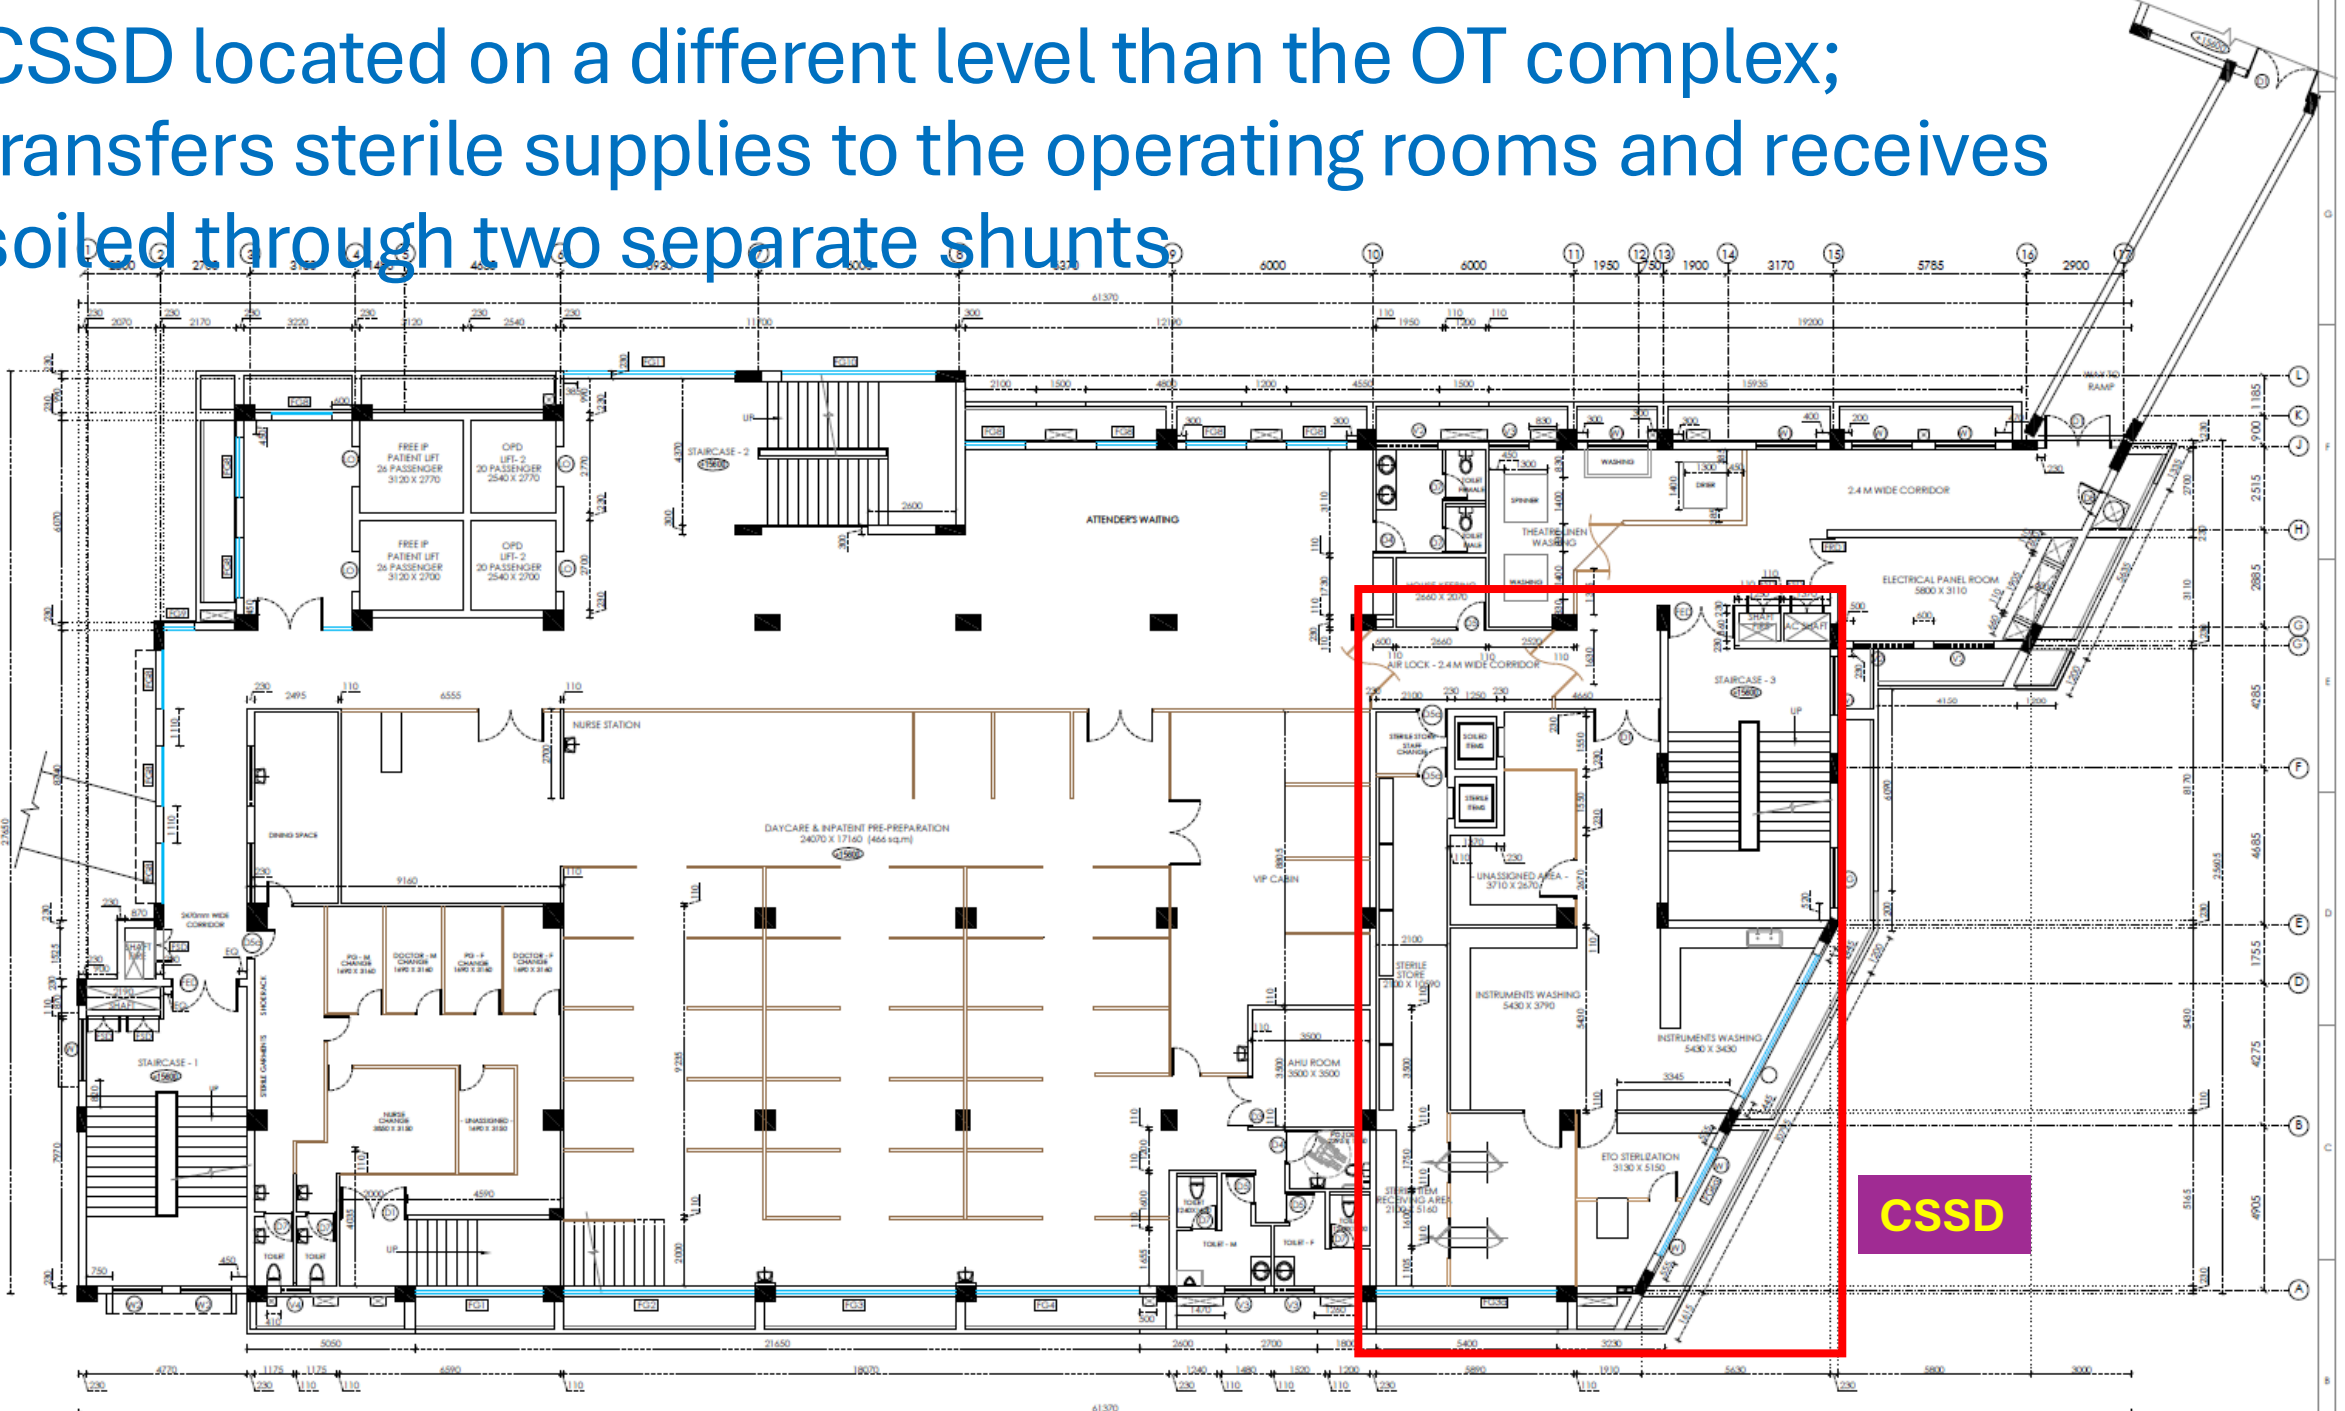

CSSD, located on a different level than the OT complex;

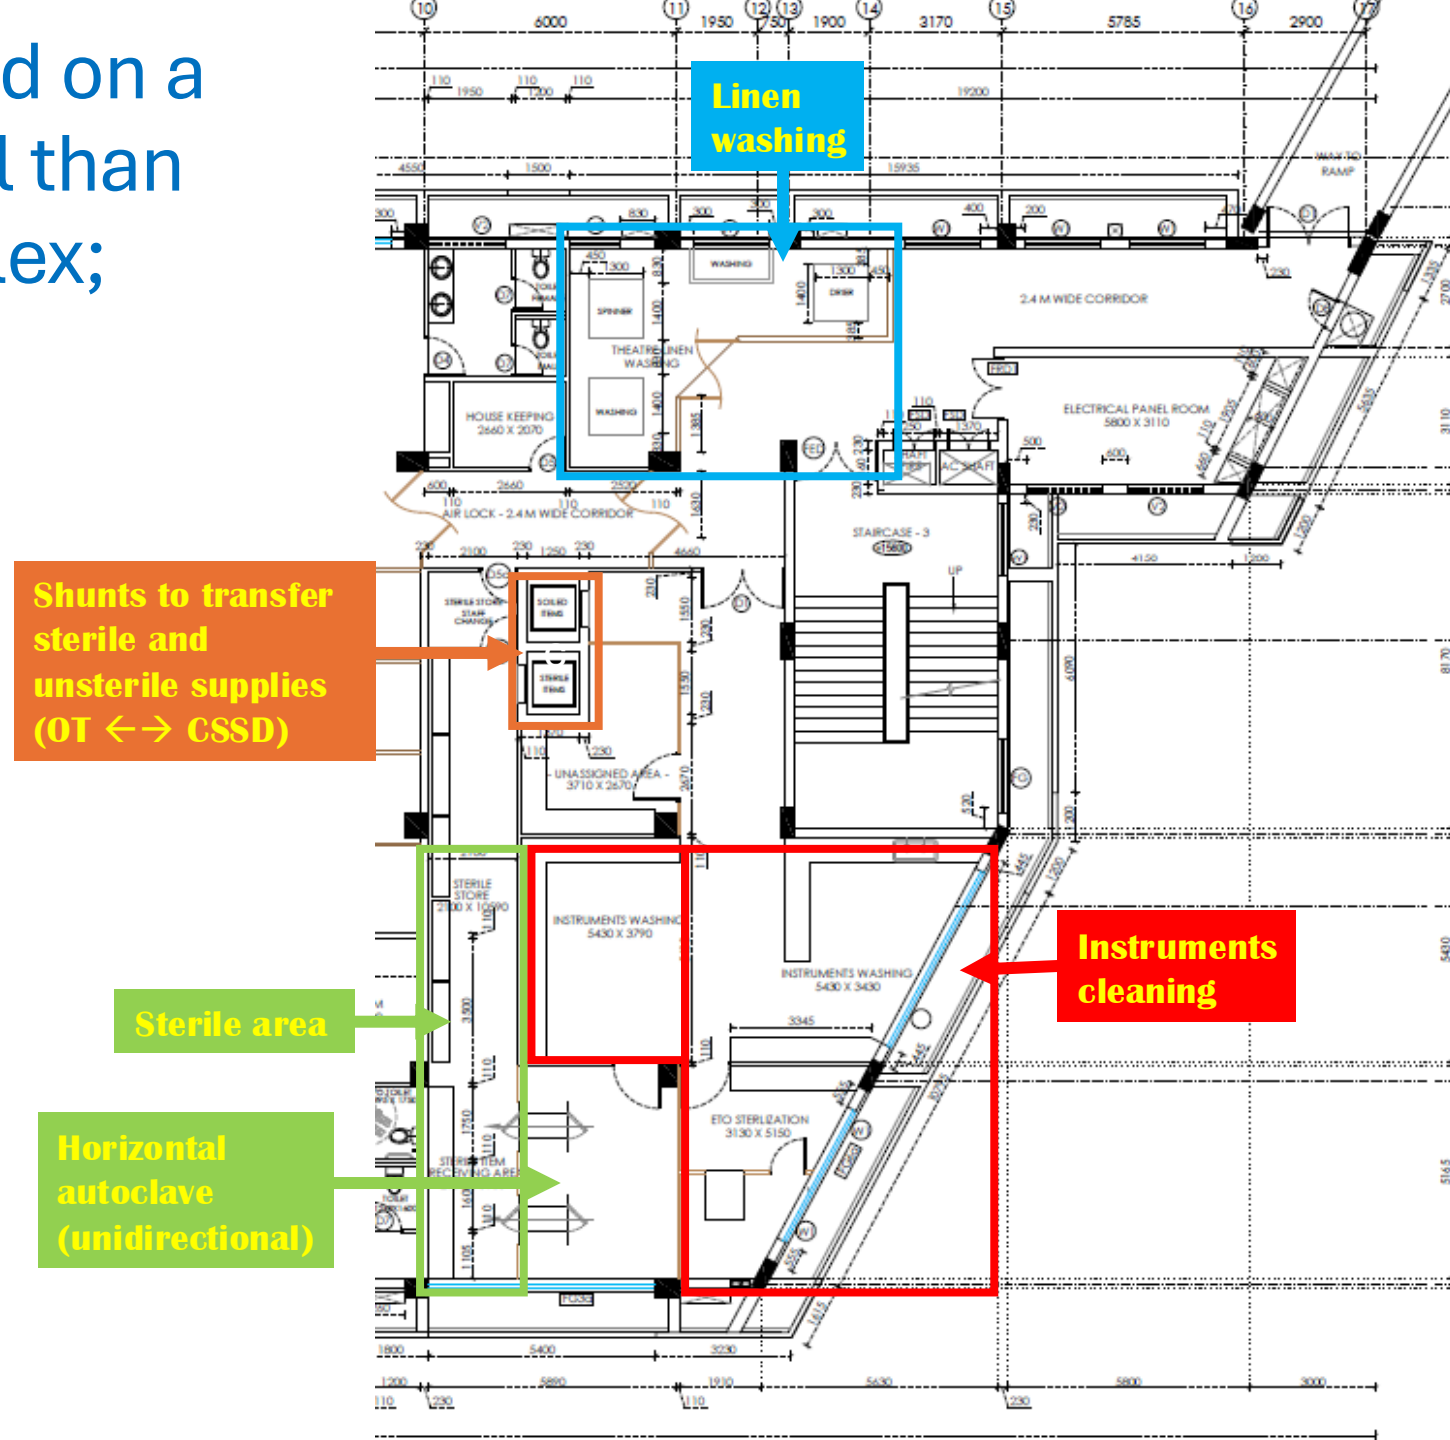

Operating rooms in the sterile zone on the next level of the building;

