


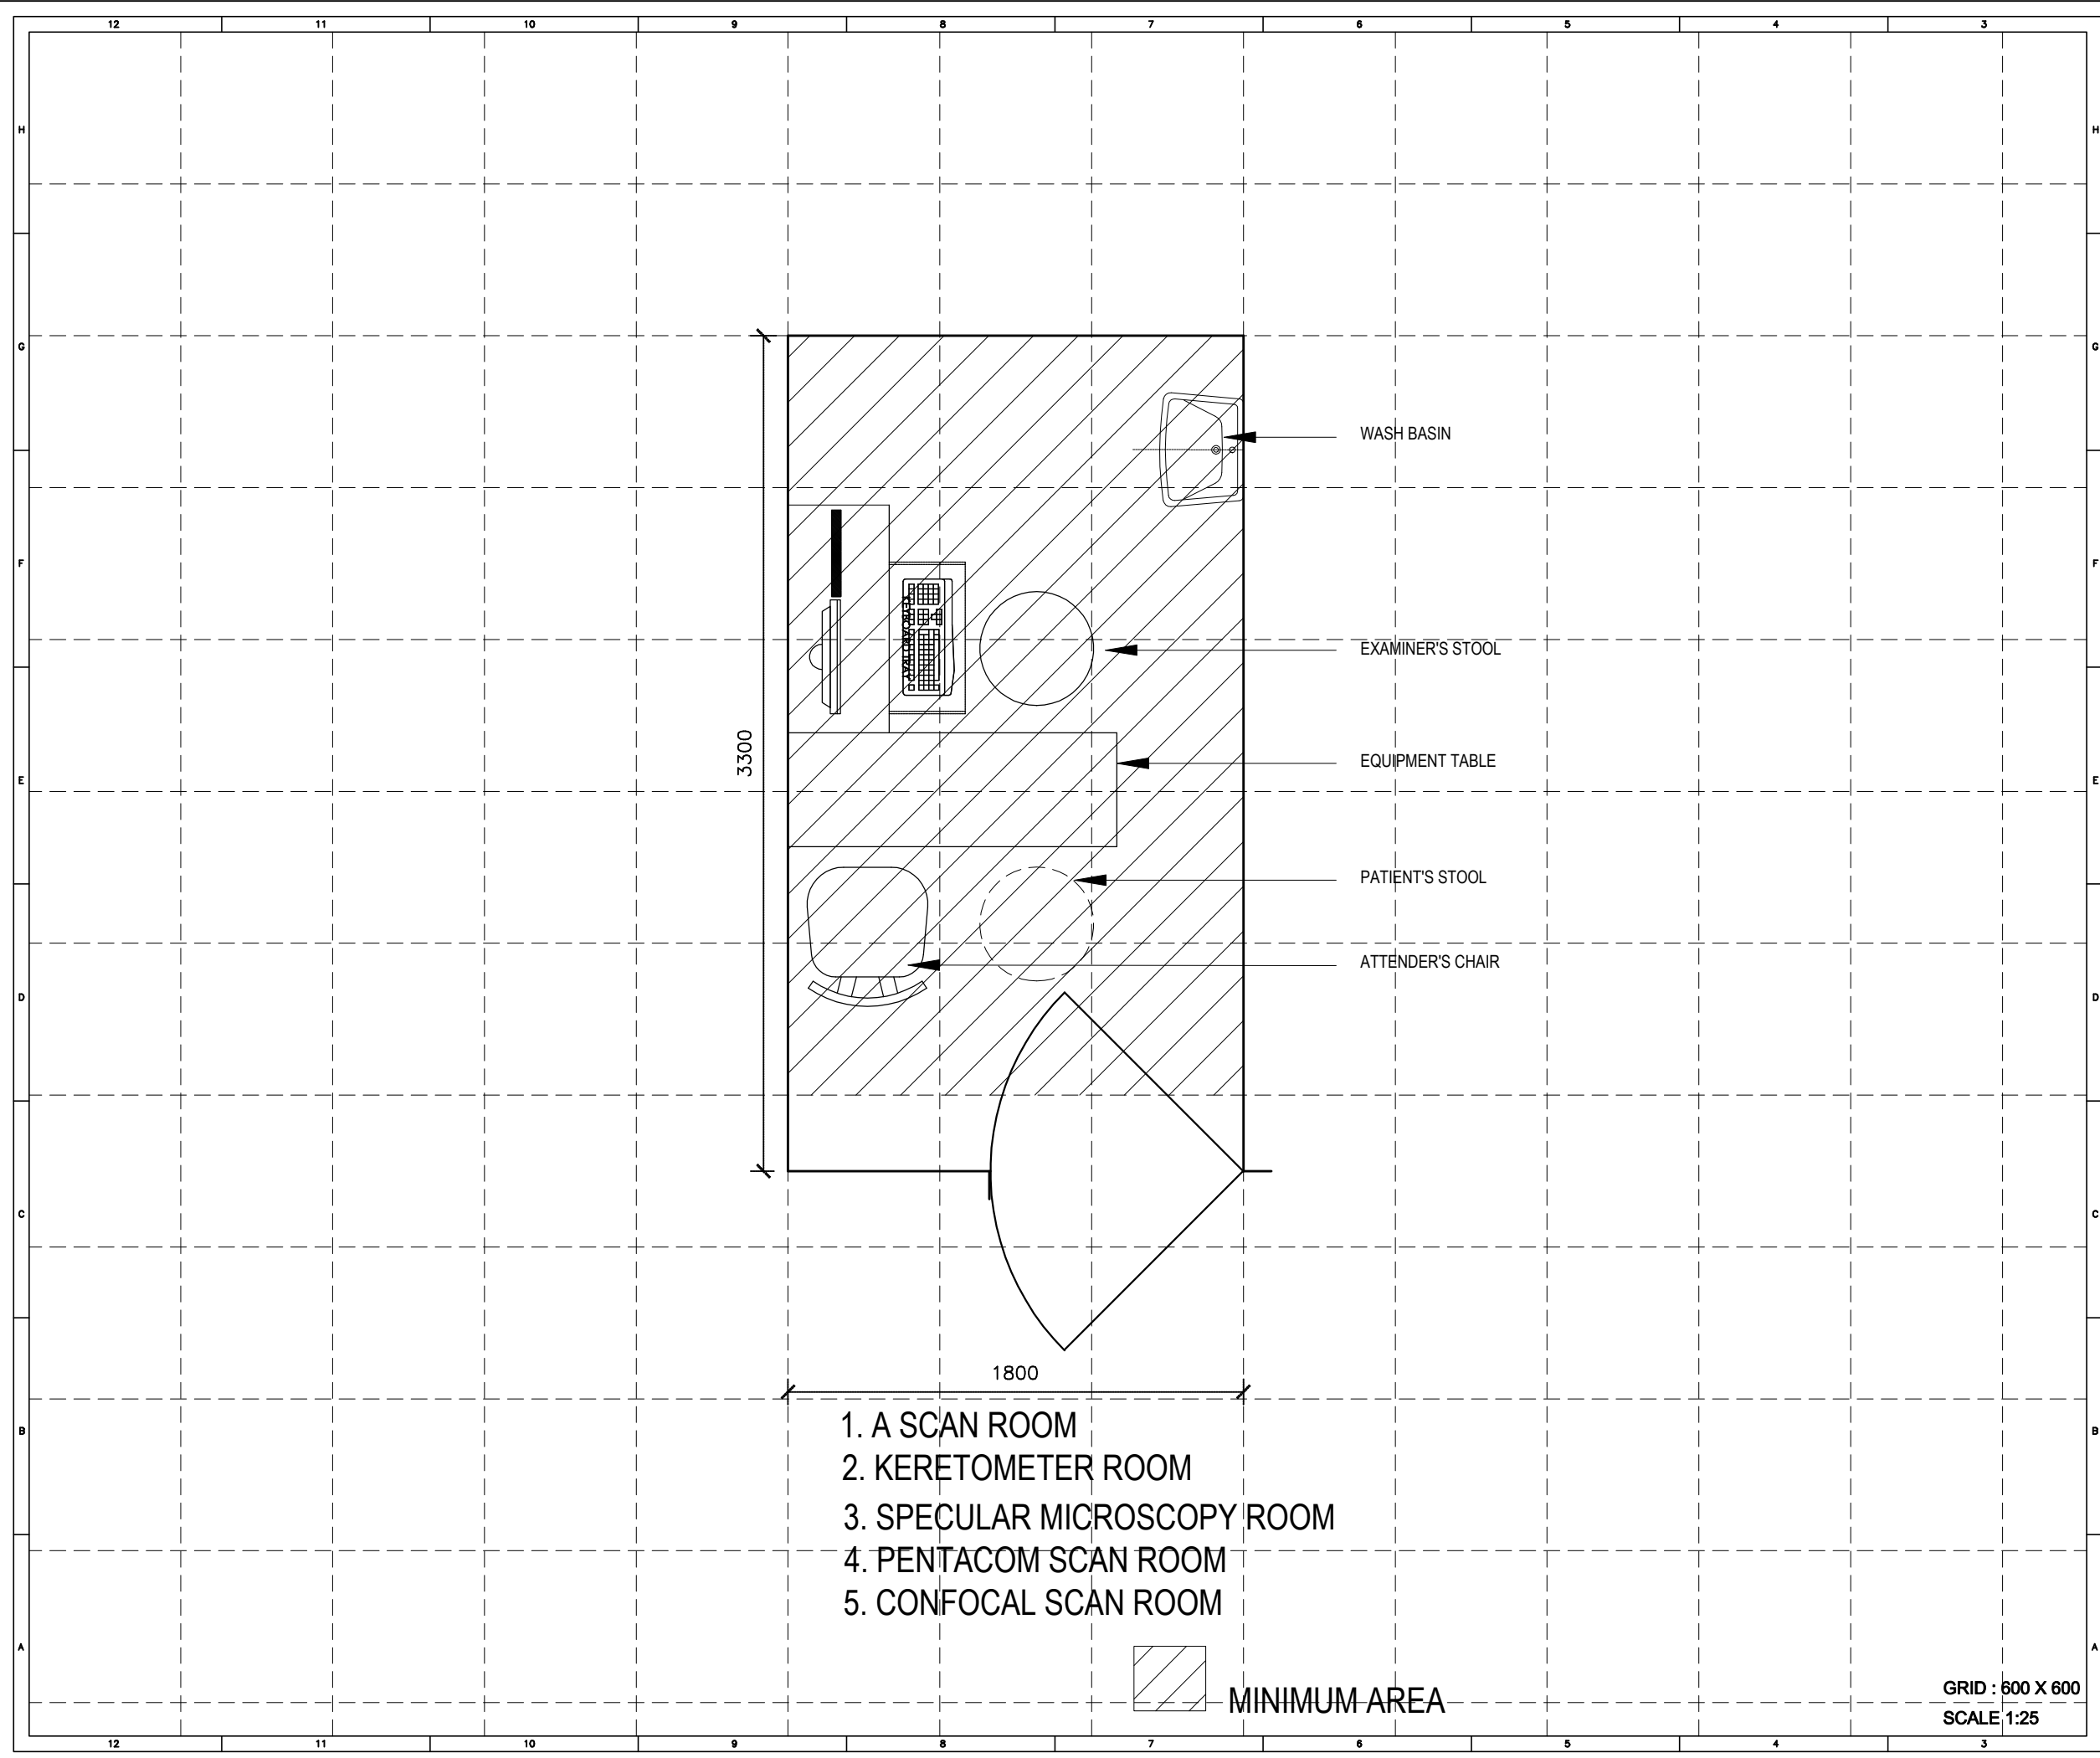

Copyright of designs shown herein is retained by this office. Authority is required for any reproduction.
Copyright DC Pte. Ltd.

- NOTES:
- All dimensions are in mm unless otherwise specified.
 - Figured dimensions are to be taken in preference to scale.
 - Latest drawing to be followed
 - Contractor to verify all dimensions on site before commencing the work.
 - Any discrepancies in the drawing to be brought to the notice of the consultants before execution.

REV	DATE	DESCRIPTION	DWN.	APP.
REVISIONS				

REFERENCES:

ARAVIND EYE HOSPITAL
STANDARDISED ARCHITECTURAL MODULES

PREFERERD LAYOUT

MULTI PURPOSE SCAN ROOM

Department	ARCHITECTURAL
Drawn	T.BRAHMANI
Dealt	I.G
Checked	I.G
Date	11.09.2014

Sheet size A 3

DESIGN COLLABORATIVE

- Architecture
- Planning
- Engineering
- Graphic Design

No.179, III Floor, S.V.Complex, Eswaran koil st., Puducherry-605 001

1240 - A-1 014 R 0